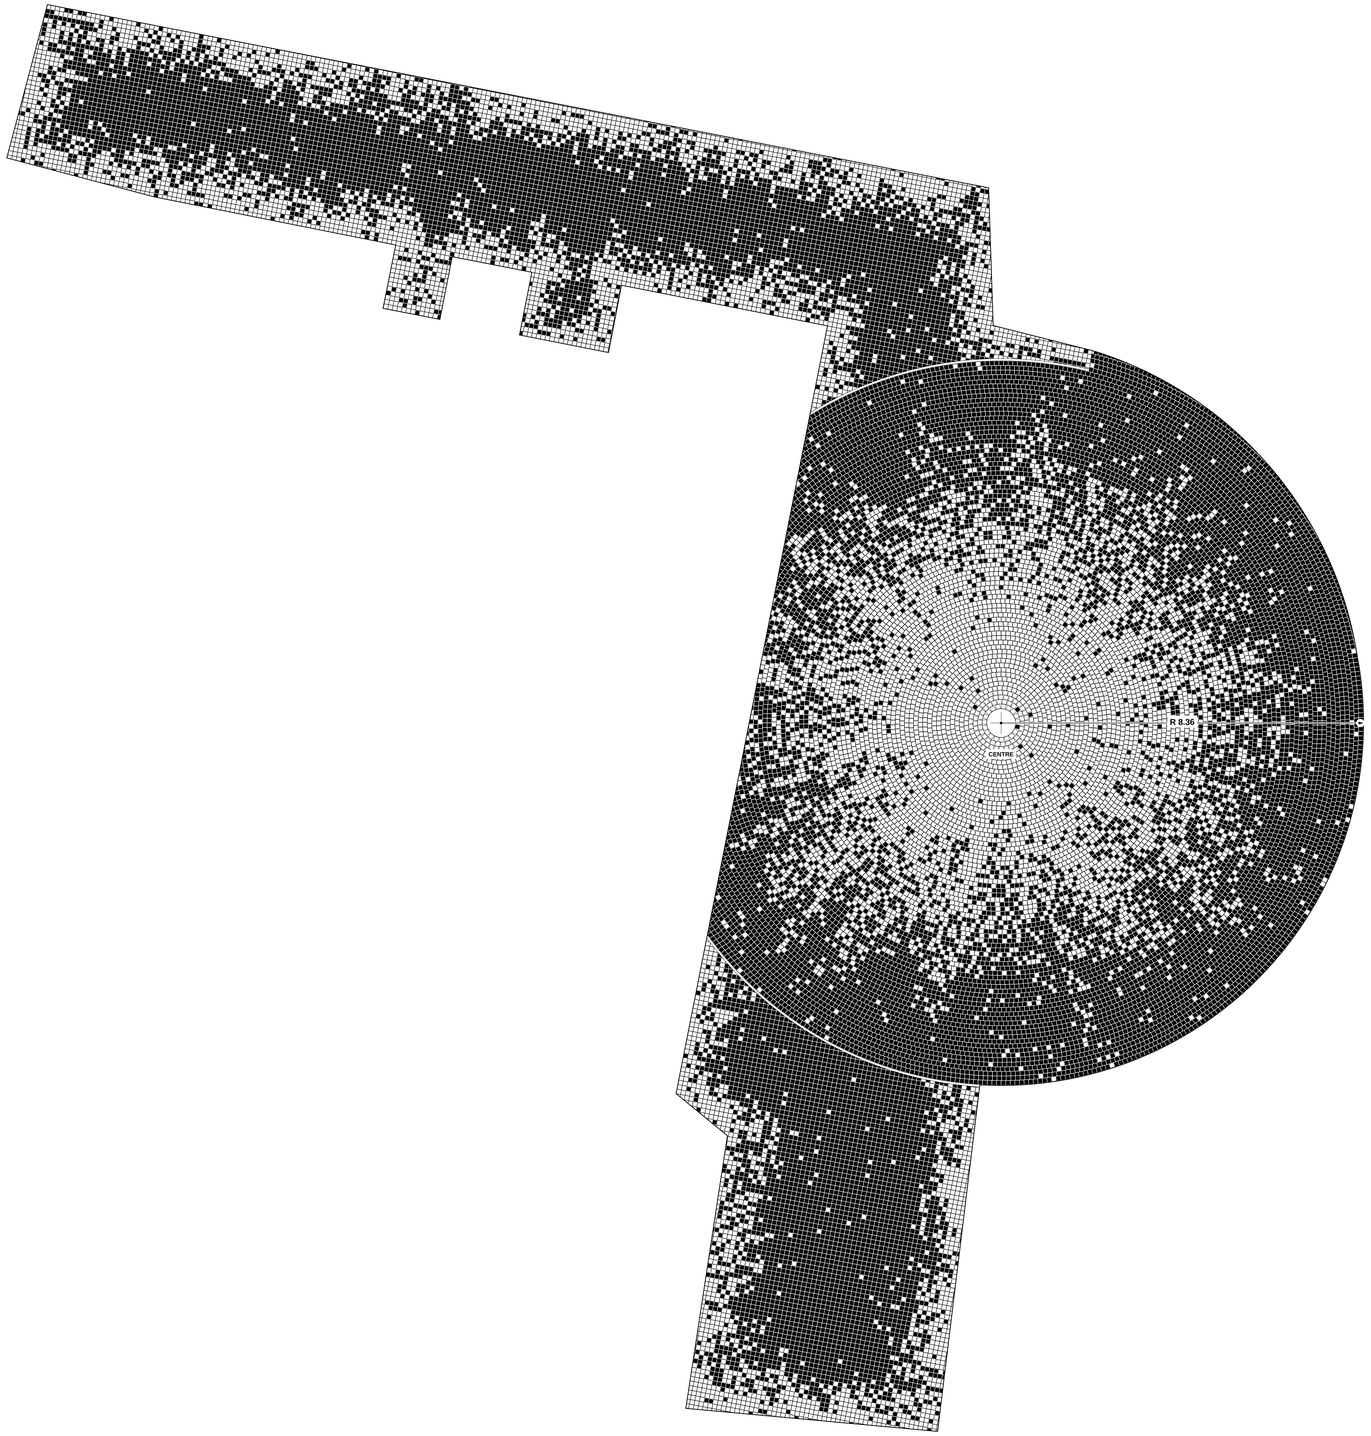


PAVER LAYOUT PLAN

Radial & linear scatter (dither) pattern

LEGEND

- Black paver, 4" x 4" (101.6 x 101.6 mm)
- White paver, 4" x 4" (101.6 x 101.6 mm)
- Plot boundary
- 50 mm edging strip at R 8.36 (plaza / linear junction)

NOTES

1. All dimensions in metres unless noted otherwise.
2. Dimensions are taken from the centre of the circle.
3. Pavers: 4" x 4" (101.6 mm) square units, 4 mm joints.
4. Circular zone: 77 concentric courses laid radially from a 0.66 m dia. centre stone out to R 8.36 / plot edge.
5. Linear zones: stack-bond grid parallel to the long plot edge; pavers cut to suit at plot boundary and edging strip.
6. Scatter: white pavers dense at the circle centre, dithering out to black toward R 8.36. In the linear zones white pavers cluster along the plot edges and fade to black over ~1.6 m.
7. Final scatter to be set out on site per this drawing.
8. Approx. quantities (incl. cut units): black 20,751, white 11,523.

SCALE 1:50 (A0)

0 1 2 3 4 5 m

Drawing: Paver layout - line drawing

Units: metres Paper: A0 Scale: 1:50

Base plot: pavers.pdf (AutoCAD)